


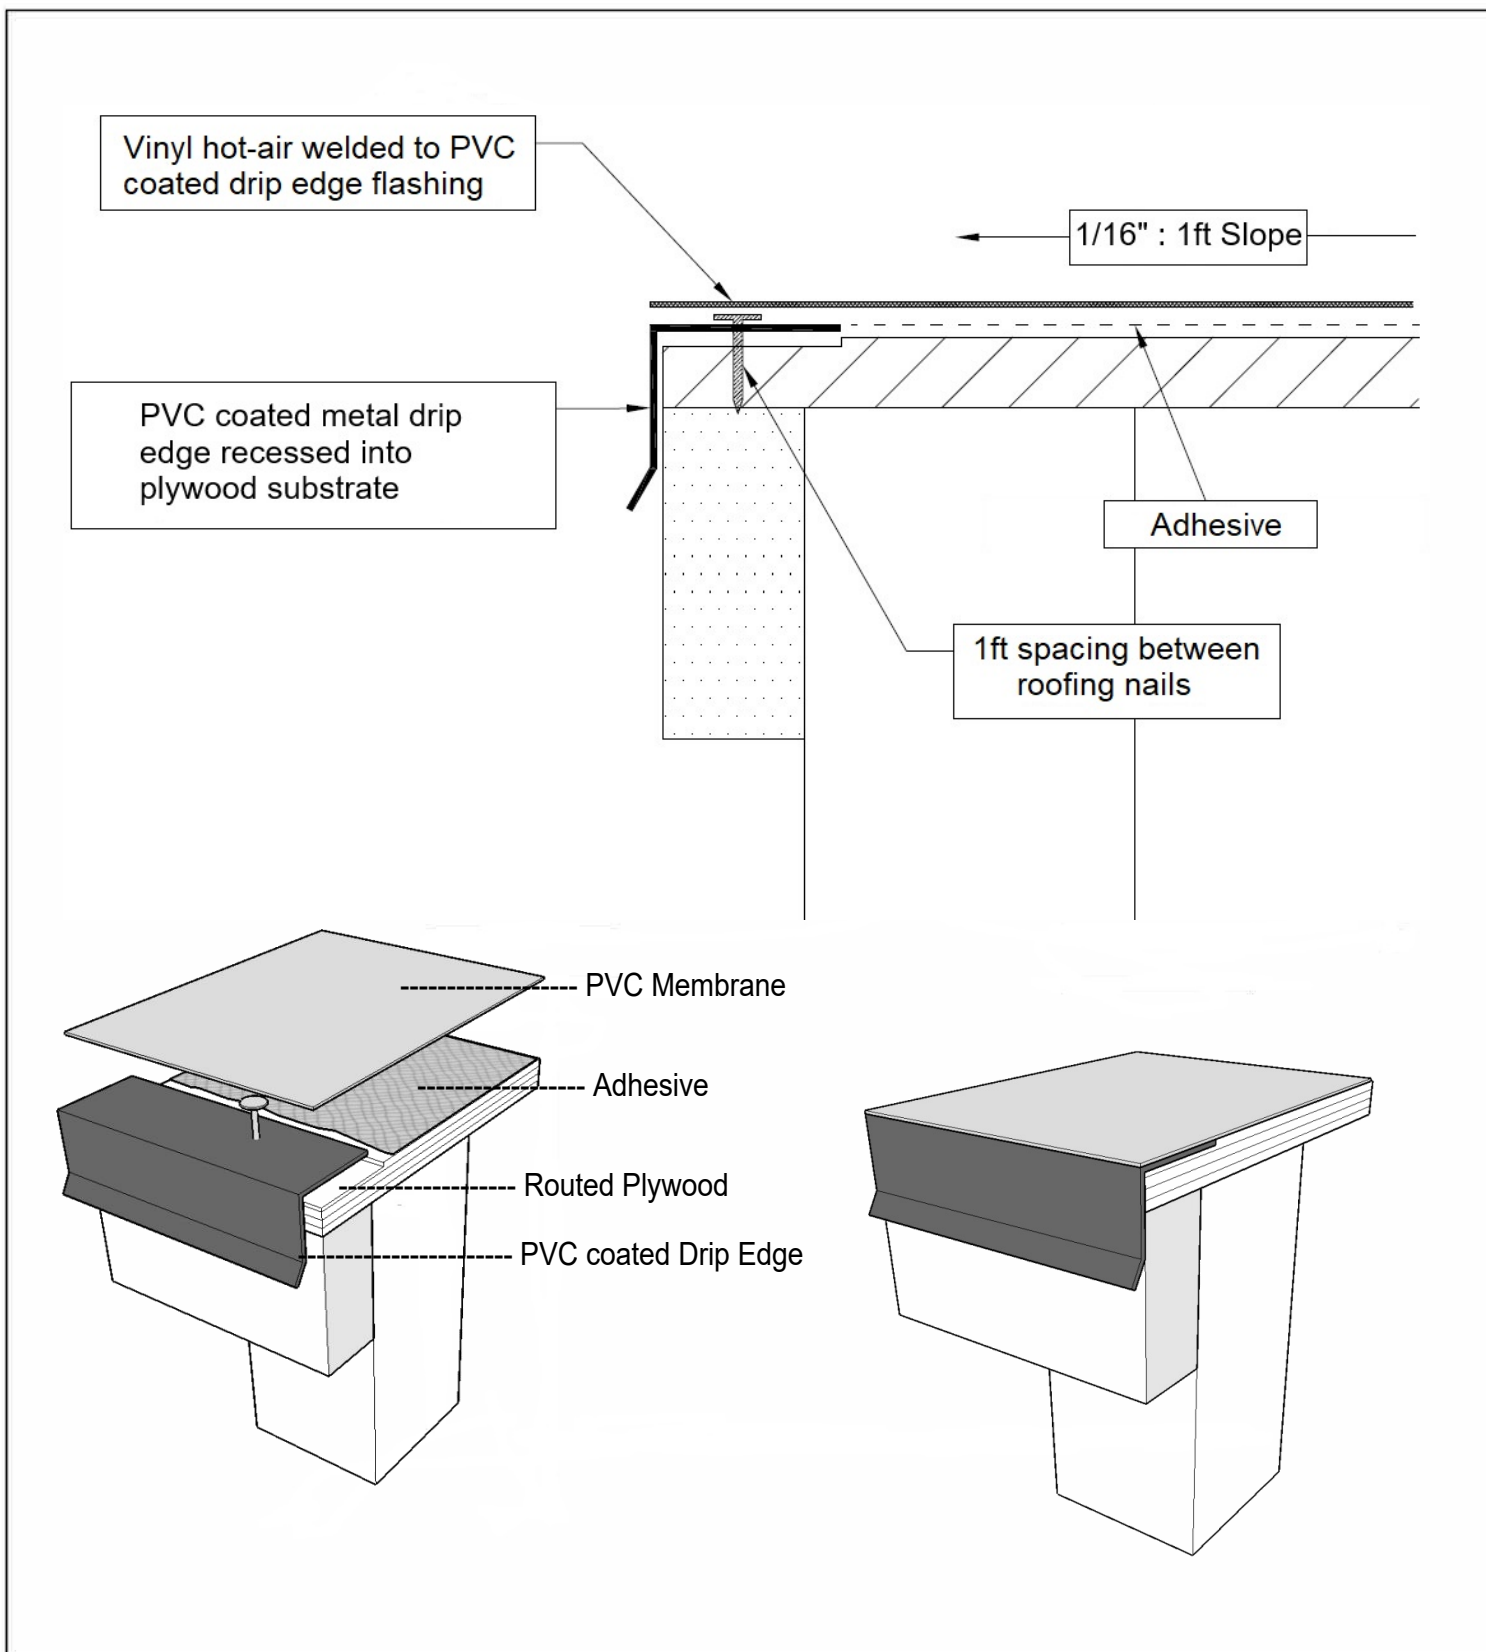

3912 E. Progress, North Little Rock, AR. 72114 Phone: (888) 450-3325

DETAIL NO.:

DR-113

DRAWING TITLE:

**DRIP EDGE FLASHING
OVER PLYWOOD**

UPDATED:

12/10/2025

SYSTEM:

FULLY ADHERED